

Согласовано:

Взам. инв. №

Подпись и дата

Инв. № подл.

Ведомость рабочих чертежей основного комплекта ПП.

Лист	Наименование	Примечание
1	Общие данные.	
2	Ситуационный план.	
3	Схема планировочной организации земельного участка М 1:1000.	
4	Сводный план инженерных сетей М 1:1000.	
5	Планы расположения земельных участков.	
6	Планы дорог 1, 2. Разрезы 1-1, 2-2.	
7	Одноквартирный двухэтажный жилой дом. 3D вид.	
8	Одноквартирный двухэтажный жилой дом. Планы 1-го и мансардного этажа.	
9	4-х квартирный 2-х этажный жилой дом. 3D вид.	
10	4-х квартирный 2-х этажный жилой дом. План 1 этажа.	
11	4-х квартирный 2-х этажный жилой дом. План 2 этажа.	
12	Здание бытового обслуживания. 3D виды.	
13	Здание бытового обслуживания. Планы 1 и 2 этажа. Фасады.	
14	Детский сад-школа на 120 мест. 3D вид.	
15	Детский сад-школа на 120 мест. План 1 этажа.	
16	Мечеть на 60 посетителей. План 1 и 2 этажа. 3D виды.	

Ведомость ссылочных и прилагаемых документов.

Обозначение	Наименование	Примечание
	Ссылочные документы.	
СП 42.13330.2016	Градостроительство. Планировка и застройка городских и сельских поселений. Актуализированная редакция СНиП 2.07.01-89*.	
СП 30-102-99	Планировка и застройка территории малоэтажного жилищного строительства.	
СНиП 2.05.02-85*	Автомобильные дороги.	
	Местные нормативы градостроительного проектирования Нижнекамского муниципального района Республики Татарстан	

Общие указания.

1. Пилотный проект коттеджного поселка, расположенного в н.п. Большое Афанасово Нижнекамского района выполнен на основании:
- задания на проектирование;

- топографической съемки проектируемого участка и прилегающих территорий, выполненной ООО "Геомастер" 11.2025 году, система координат МСК-16, система высот - Балтийская;


-архитектурно-планировочного задания;
2. Плановая привязка проектируемого объекта дана к координатной сетке в системе топоплана.
3. Рабочие чертежи разработаны в соответствии с заданием на проектирование, требованиями действующих технических регламентов, стандартов, сводов правил, других документов содержащих установленные требования.
4. Все размеры даны в метрах.

Условные обозначения.

- границы проектируемой территории
- границы водоохранных зон
- проектируемые участки с 1 квартирными жилыми домами;
- проектируемые участки 4-х квартирными жилыми домами (таунхаусы)
- асфальтобетонное покрытие подъездных дорог, с щебеночным основанием;
- границы охранных зон газопровода низкого давления
- границы охранных зон ЛЭП 10 кВ
- зеленая зона

						01/26 - ПП		
						Пилотный проект коттеджного поселка в н.п. Б. Афанасово Нижнекамского района		
Изм.	Кол.	Лист	№ док	Подпись	Дата	Пилотный проект коттеджного поселка	Стадия	Лист
Разраб.		Азлетдинова					П	1
Проверил		Катаева						16
ГИП		Катаева				Общие данные.	АО "Нижнекамский Татагропромпроект"	
Н. контр.		Наурова						
Гл. инж.		Ибрагимова						


Ситуационный план.

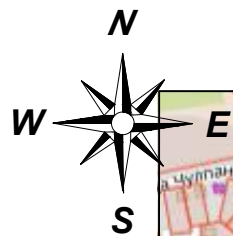

Согласовано:		Взам. инв. №	Подпись и дата	Инв. № подл.

						01/26 - ПП			
						Пилотный проект коттеджного поселка в н.п. Б. Афанасово Нижнекамского района			
Изм.	Кол.	Лист	№ док	Подпись	Дата	Пилотный проект коттеджного поселка	Стадия	Лист	Листов
Разраб.		Азлетдинова					П	2	
Проверил		Катаева							
ГИП		Катаева				Ситуационный план.		АО "Нижнекамский Татагропромпроект"	
Н. контр.		Нацурова							
Гл. инж.		Ибрагимова							

Пилотный проект коттеджного поселка
в н.п. Большое Афанасово.

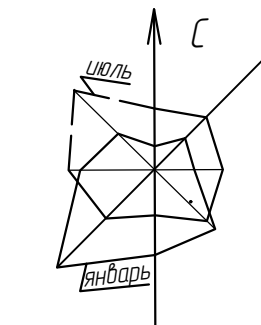


Экспликация зданий и сооружений.

№ по ГП	Наименование	Кол.	Примечание
1	Жилая зона под многоквартирный 2-х этажный жилой дом	47	проект.
2	Жилая зона под 4-х квартирный 2-х этажный дом (таунхаус)	35	проект.
3	Мечеть на 60 поселителей.	1	проект.
4	Детский сад на 60 мест	1	проект.
5	Средняя школа на 60 учащихся.	1	проект.
6	Здание бытового обслуживания.	1	проект.
7	Стоянка на 20 автомашин на территории мечети.	1	проект.
8	Стоянка на 23 автомашин общая по всей территории.	1	проект.
9	Водонапорная стальная башня с артезианскими скважинами.	1	проект.
10	Территория под лифтовые очистные сооружения	1	проект.
11	Спортивная площадка.	1	проект.
12	Детская площадка.	1	проект.
13	ГРПШ.	1	проект.
14	КТП на 2 трансформатора х 630 кВа.	1	проект.
15	Мост через ручей.	1	перспек.

Техника – экономические показатели.

Наименование	Площадь	
	м ²	%
Общая площадь территории	21700 (2171,20)	100
Общая площадь участков под коттеджную застройку	97530,06	44,92
в т.ч. под 1-квартирные жилые дома	46064,15	21,22
в т.ч. под 4-х квартирные таунхаусы	51465,91	23,70
Площадь участков под объекты социальной инфраструктуры (территория школы с детским садом, территории под здание бытового обслуживания с магазином, территория под мечеть)	7624,64	3,51
Площадь участков под инженерные сооружения (КТП, ГРПШ)	148,00	0,07
Площадь участка с твердым покрытием (улицы, стоянки, проезды, пешеходные дорожки)	40592,00	18,70
Площадь участков под озеленение (включая площадь детских и спортивных площадок, защитной зоны артезианских скважин, подземных очистных сооружений)	71205,36	32,80

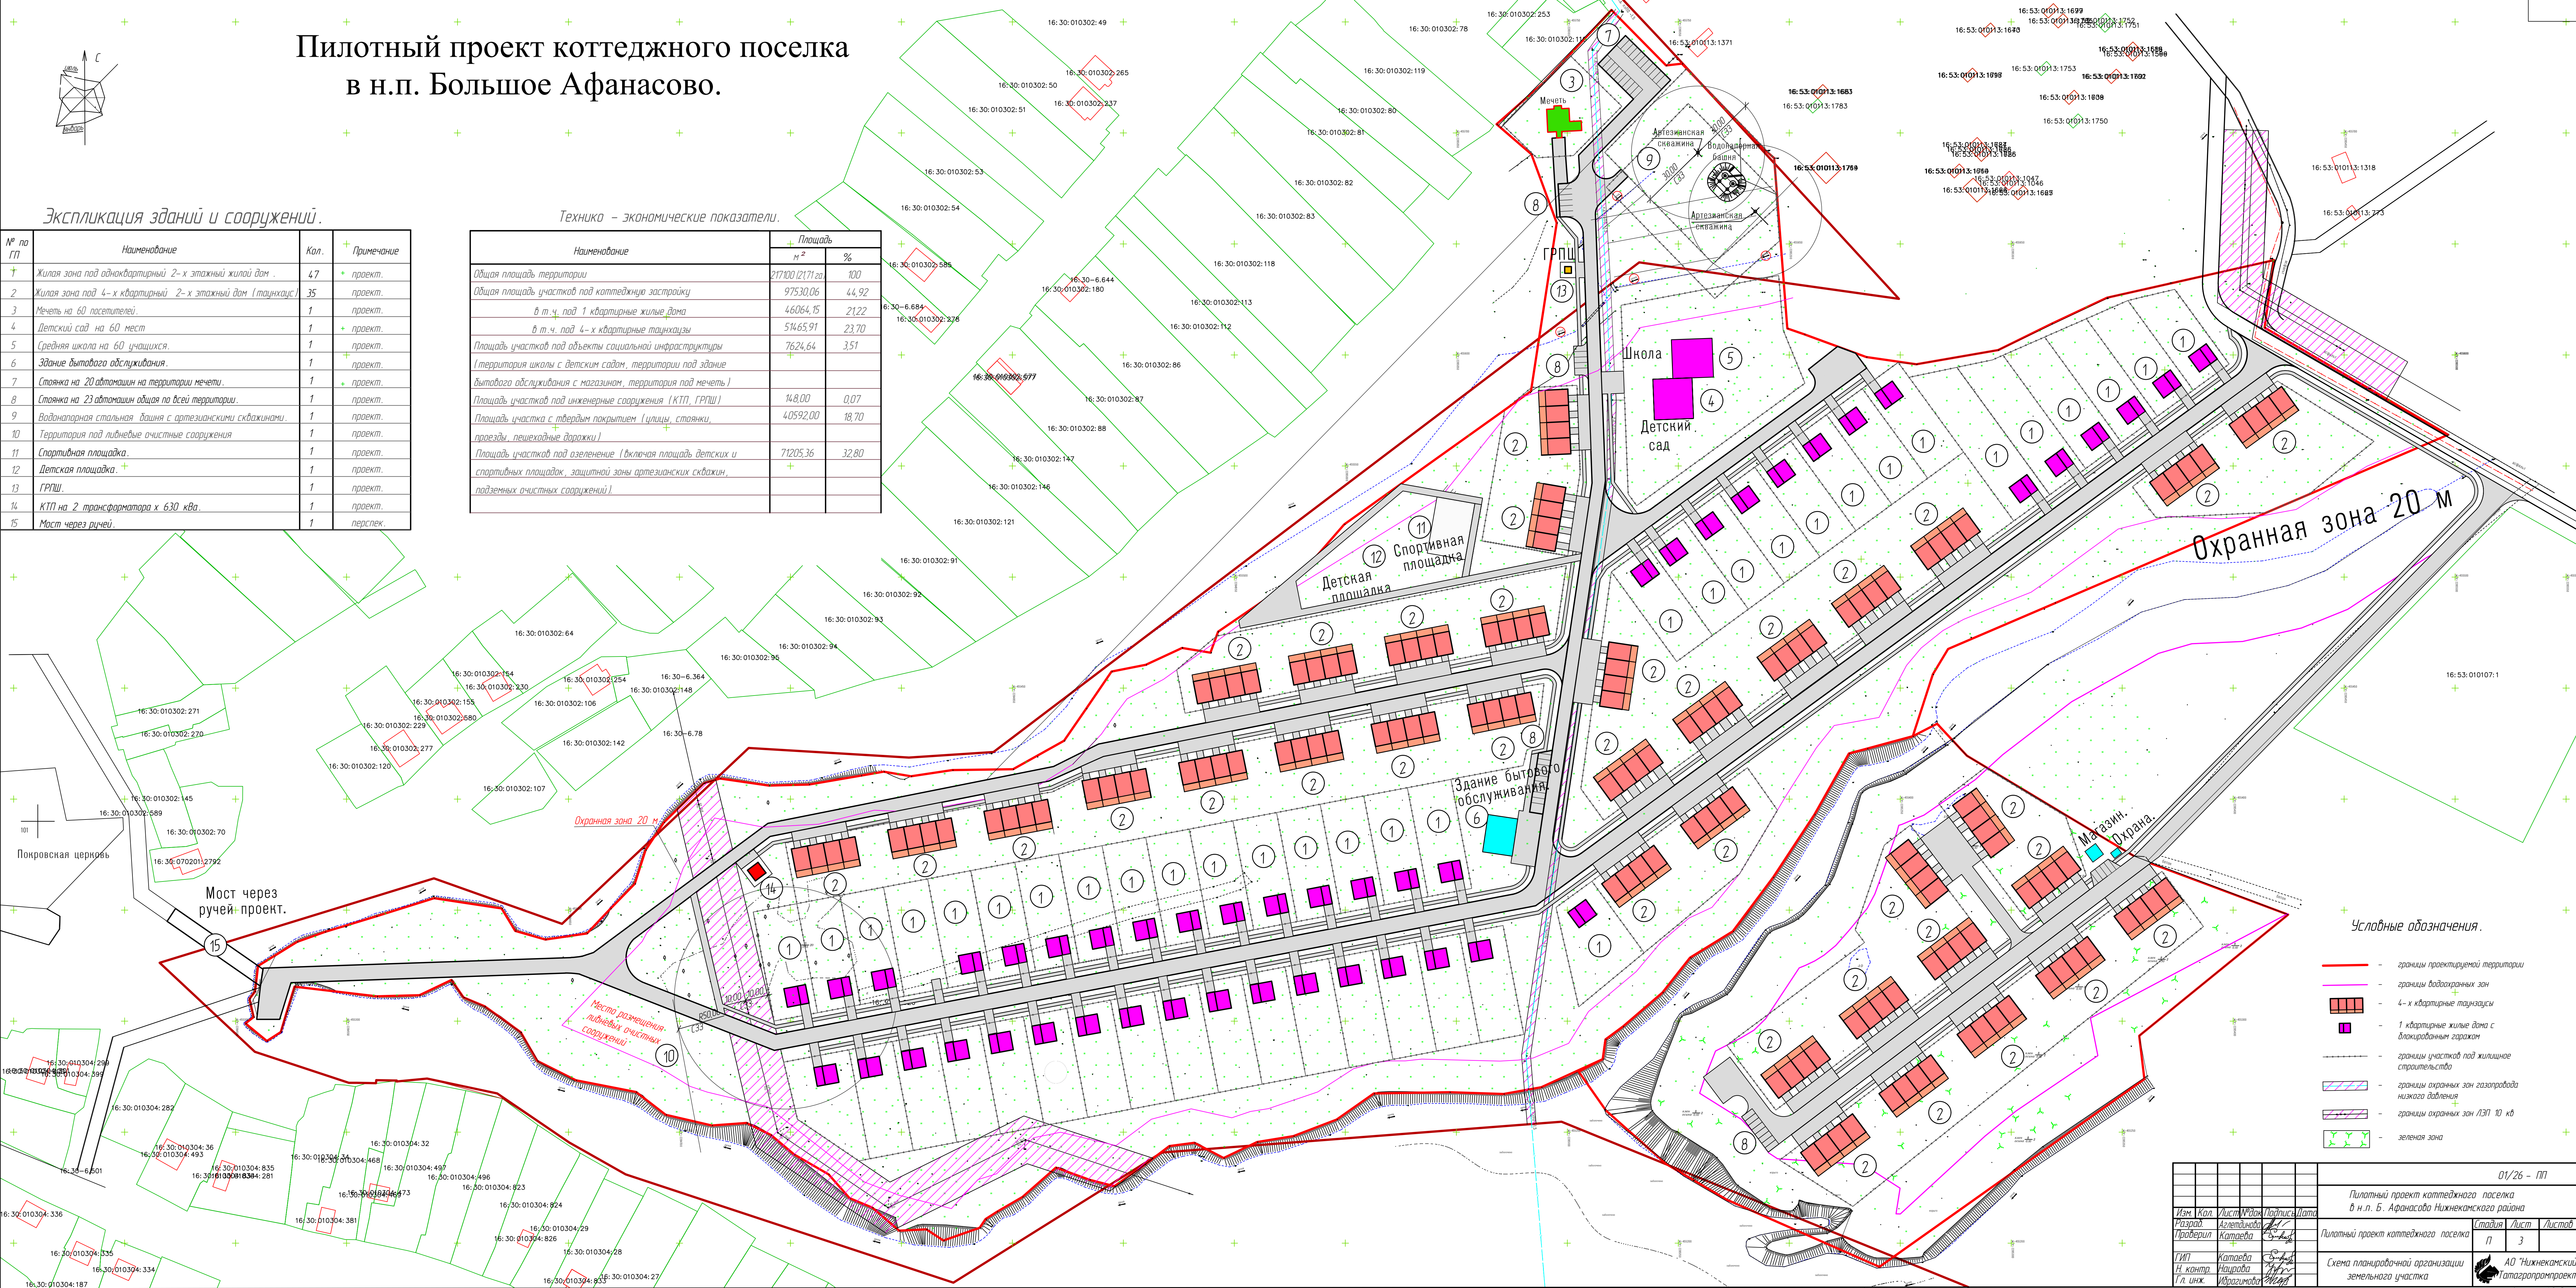

Условные обозначения.


- границы проектируемой территории
- границы водоохранных зон
- 4-х квартирные таунхаусы
- 1-квартирные жилые дома с блокированным гаражом
- границы участков под жилищное строительство
- границы охранных зон газопровода низкого давления
- границы охранных зон ЛЭП 10 кВ
- зеленая зона

						01/26 – ПП		
						Пилотный проект коттеджного поселка в п.п. Б. Афанасово Нижегородского района		
Изм.	Кол.	Лист	Масштаб	Подпись	Дата			
Разработчик			А.С.Сидоров		2024			
Проверил			К.А.Сидорова			Пилотный проект коттеджного поселка	Страница П	Лист 3
ГИП			Котова					
Н. контр.			Наумова			Схема планировочной организации земельного участка		АО "Нижегородский Таунхауспроект"
Гл. инж.			Ибрагимова					


Согласовано:

Инв. № подл. Подпись и дата Взам. инв. №


План дорог 1.

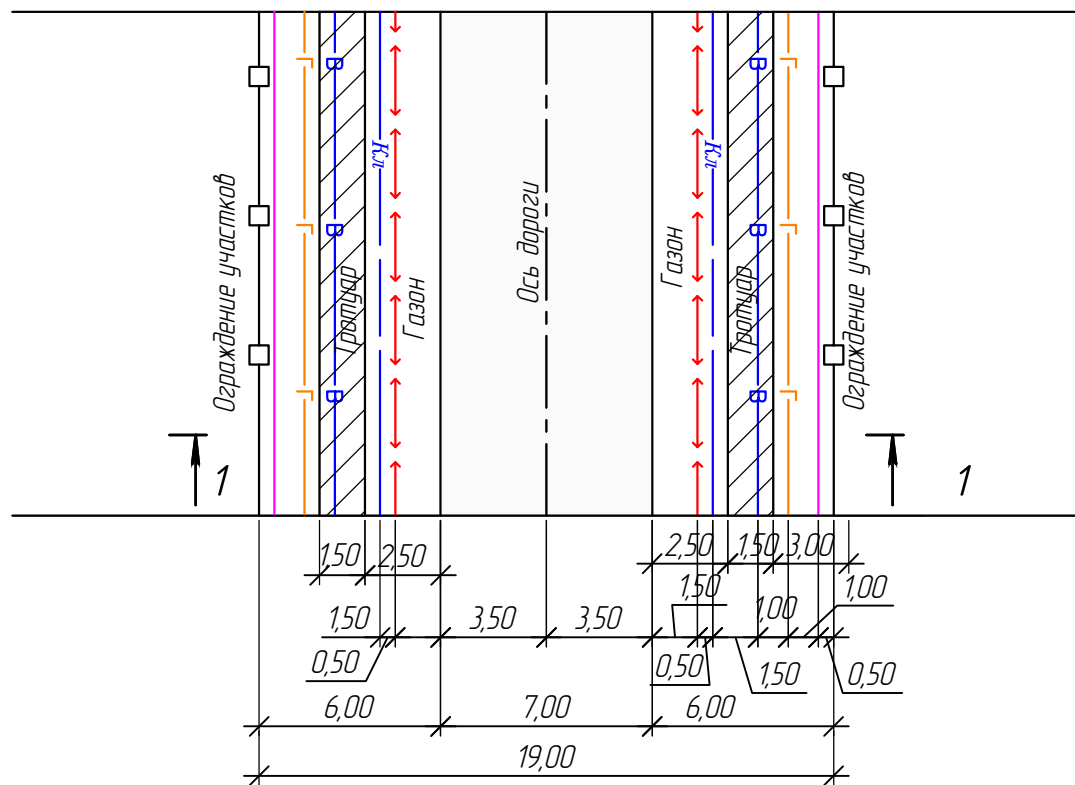


Разрез 1-1.

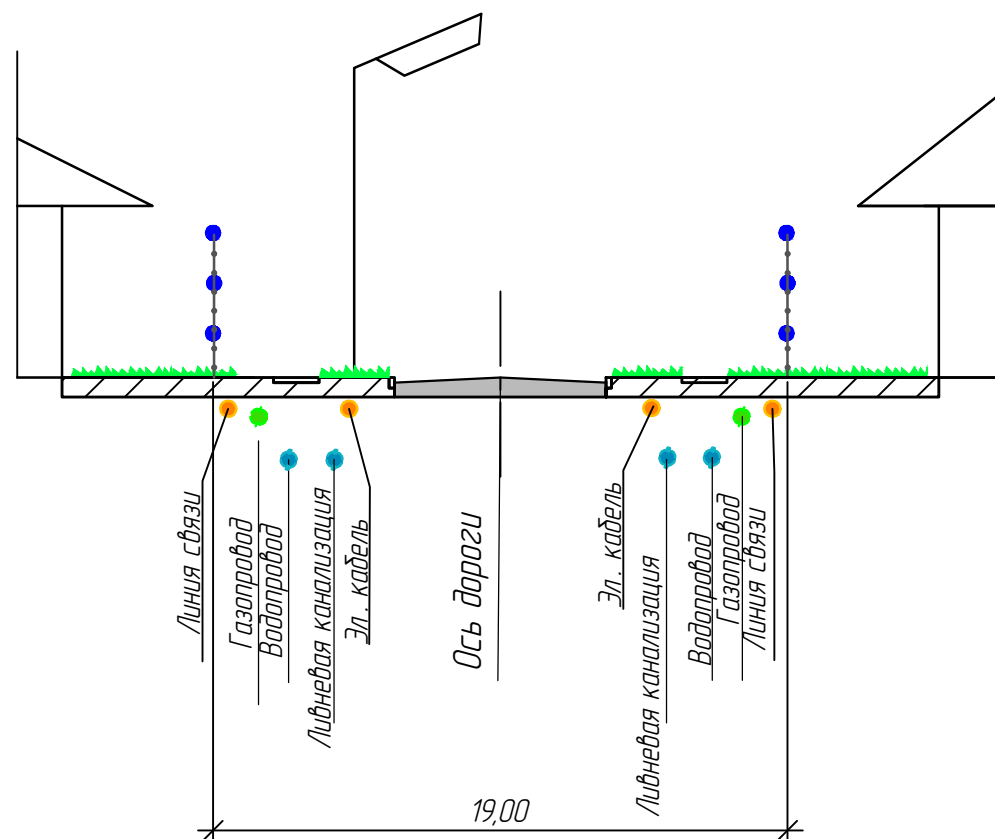

План дорог 2.

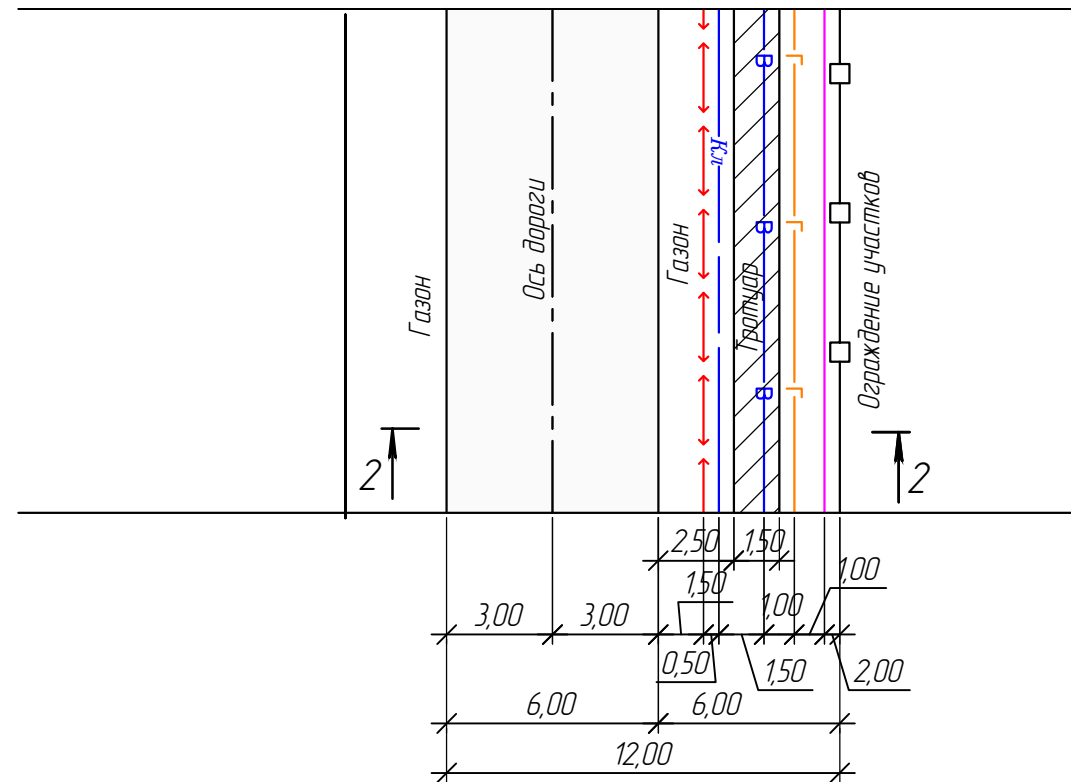

Разрез 2-2.

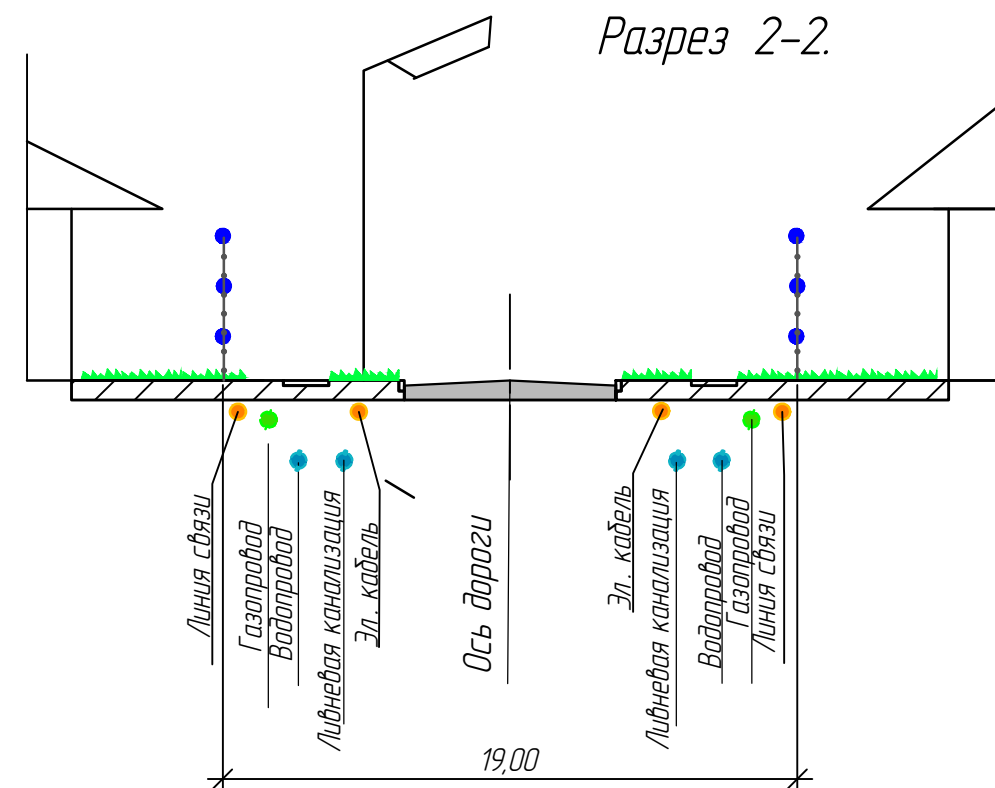

						01/26 - ПП		
						Пилотный проект коттеджного поселка в н.п. Б. Афанасово Нижнекамского района		
Изм.	Кол.	Лист	№ док	Подпись	Дата	Пилотный проект коттеджного поселка	Стадия	Лист
Разраб.		Азлетдинава					П	6
Проверил		Катаева						
ГИП		Катаева						
Н. контр.		Наурова						
Гл. инж.		Ибрагимова						
						Планы дорог 1, 2. Разрезы 1 - 1, 2 - 2.		
						АО "Нижнекамский Татагропромпроект"		


Одноквартирный двухэтажный жилой дом.
3D вид.




Наружные стены – газобетон 400 мм.
Отделка фасада – облицовочный материал
Полы – деревянные по лагам.
Кровля – битумная черепица
Фундаменты – ленточные сборные ж / б

						01/26 – ПП			
						Пилотный проект коттеджного поселка в н.п. Б. Афанасово Нижнекамского района			
Изм.	Кол.	Лист	№ док	Подпись	Дата	Одноквартирный двухэтажный жилой дом.	Стадия	Лист	Листов
Разраб.		Азлетдинава					П	7	
Проверил		Катаева				3D вид.	 АО "Нижнекамский Татагропромпроект"		
ГИП		Катаева							
Н. контр.		Нацурова							
Гл. инж.		Ибрагимова							

План первого этажа

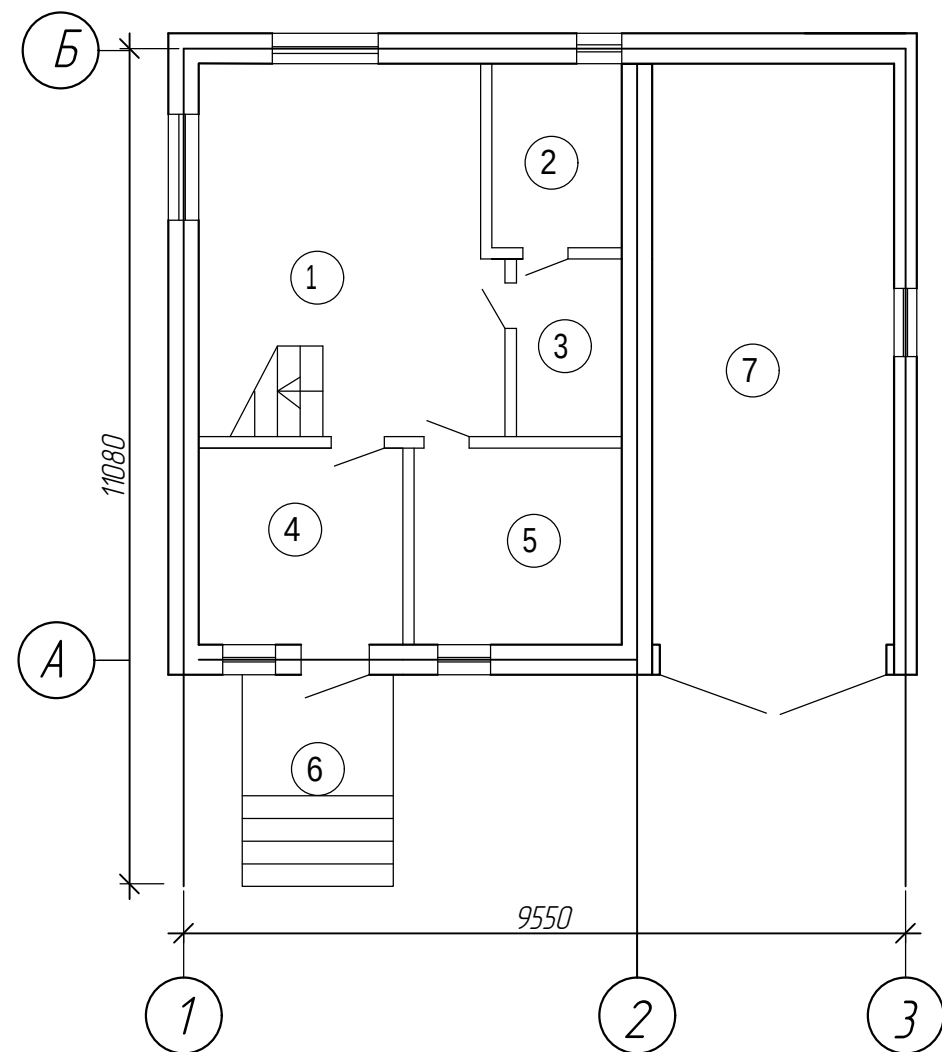

План мансардного этажа

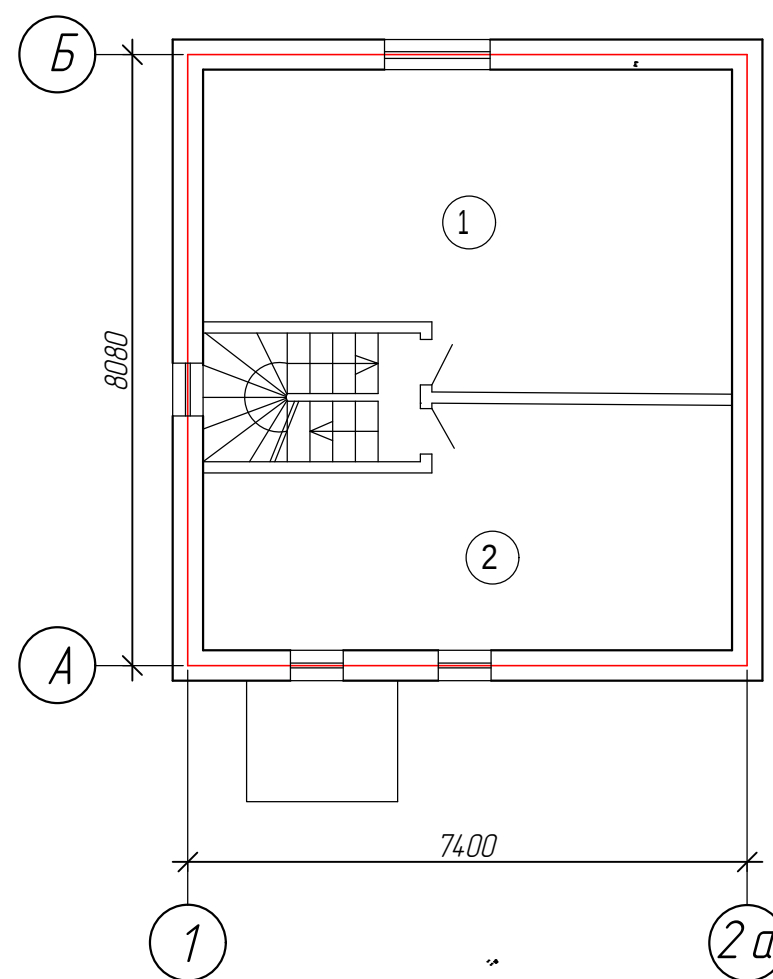

Общая площадь - 96,20 м²
Жилая площадь - 54,80 м²
Общие габариты - 9,58 x 9,55 м
Площадь застройки - 77,20 м²
Внутренняя площадь - 92,20 м²
Балконы и терраса - 4 м²
Площадь гаража - 14,30 м²
Высота 1 этажа - 2,80 м
Высота мансардного этажа - 2 / 3,43 м
Высота дома - 7,90 м

Экспликация помещений первого этажа


№ пом.	Наименование	Площадь м ²	Кат. пом.
1	Гостиная	19,0	
2	Сауна	4,8	
3	Душевая	3,4	
4	Прихожая	7,4	
5	С / у	5,9	
6	Крыльцо	4,0	
7	Гараж	14,2	

Экспликация помещений мансардного этажа

№ пом.	Наименование	Площадь м ²	Кат. пом.
1	Комната	19,5	
2	Комната	16,3	

Изм.	Кол.	Лист	№ док.	Подпись	Дата	01/26 - ПП			
Разраб.	Азлетдинава					Пилотный проект коттеджного поселка в н.п. Б. Афанасово Нижнекамского района			
Проверил	Катаева					Одноквартирный двухэтажный жилой дом	Стадия	Лист	Листов
							П	8	
ГИП	Катаева					Планы 1 и 2 этажей	 АО "Нижнекамский Татагропромпроект"		
Н. контр.	Наурова								
Гл. инж.	Ибрагимова								

План первого этажа

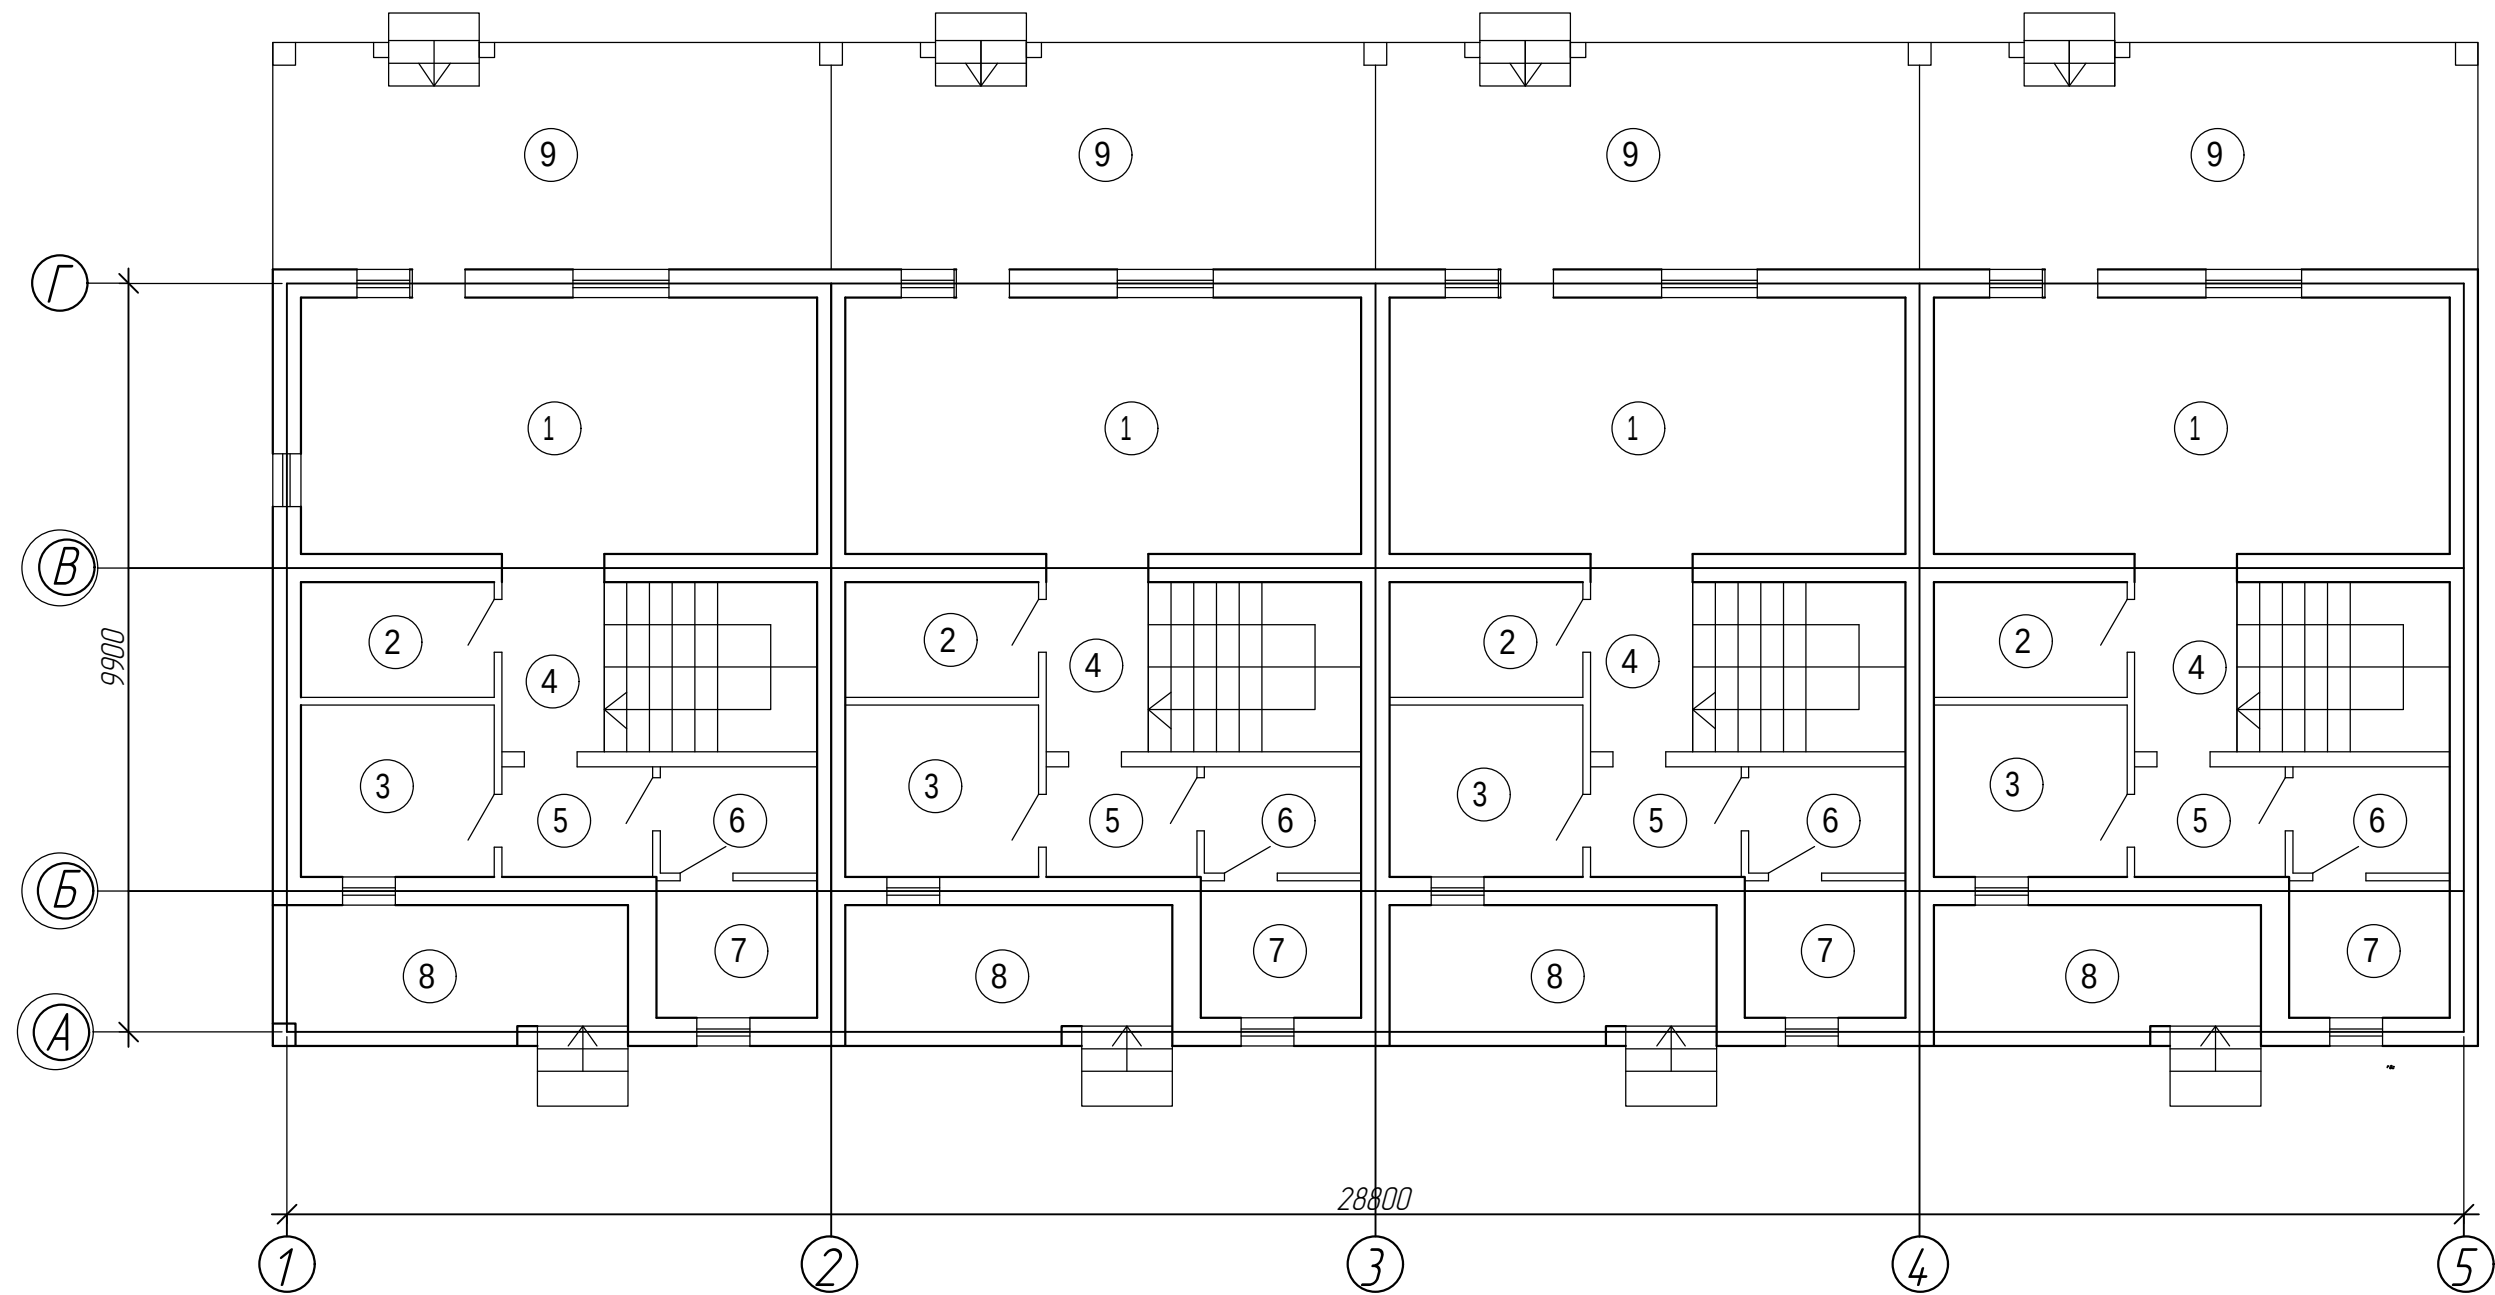


Экспликация помещений первого этажа

№ пом.	Наименование	Площадь, м²	Кат. пом.
1	Кухня -Гостиная	24,5	
2	С / у	4,6	
3	Котельная	5,7	
4	Холл	2,5	
5	Комната №1	2,7	
6	Комната №2	3,0	
7	Комната №3	2,7	
8	Крыльцо	5,8	
9	Терраса	20,3	

Полезная площадь (общ.) - 401,00 м²
Жилая площадь - 70,60 м² х 4=282,40 м²
Площадь застройки - 387,30 м²
Общие габариты - 28,80 х 9,90 м
Балконы и терраса - 104,00 м²
Высота этажей - 2,80 м
Подвал, цокольный этаж - нет





						01/26 - ПП			
						Пилотный проект коттеджного поселка в н.п. Б. Афанасово Нижнекамского района			
Изм.	Кол.	Лист	№ док	Подпись	Дата	4-х квартирный 2-х этажный жилой дом (таунхаус)	Стадия	Лист	Листов
Разраб.		Азлетдинава					П	9	
Проверил		Катаева				План 1-го этажа.	 АО "Нижнекамский Татагропромпроект"		
ГИП		Катаева							
Н. контр.		Наурова							
Гл. инж.		Ибрагимова							

План второго этажа

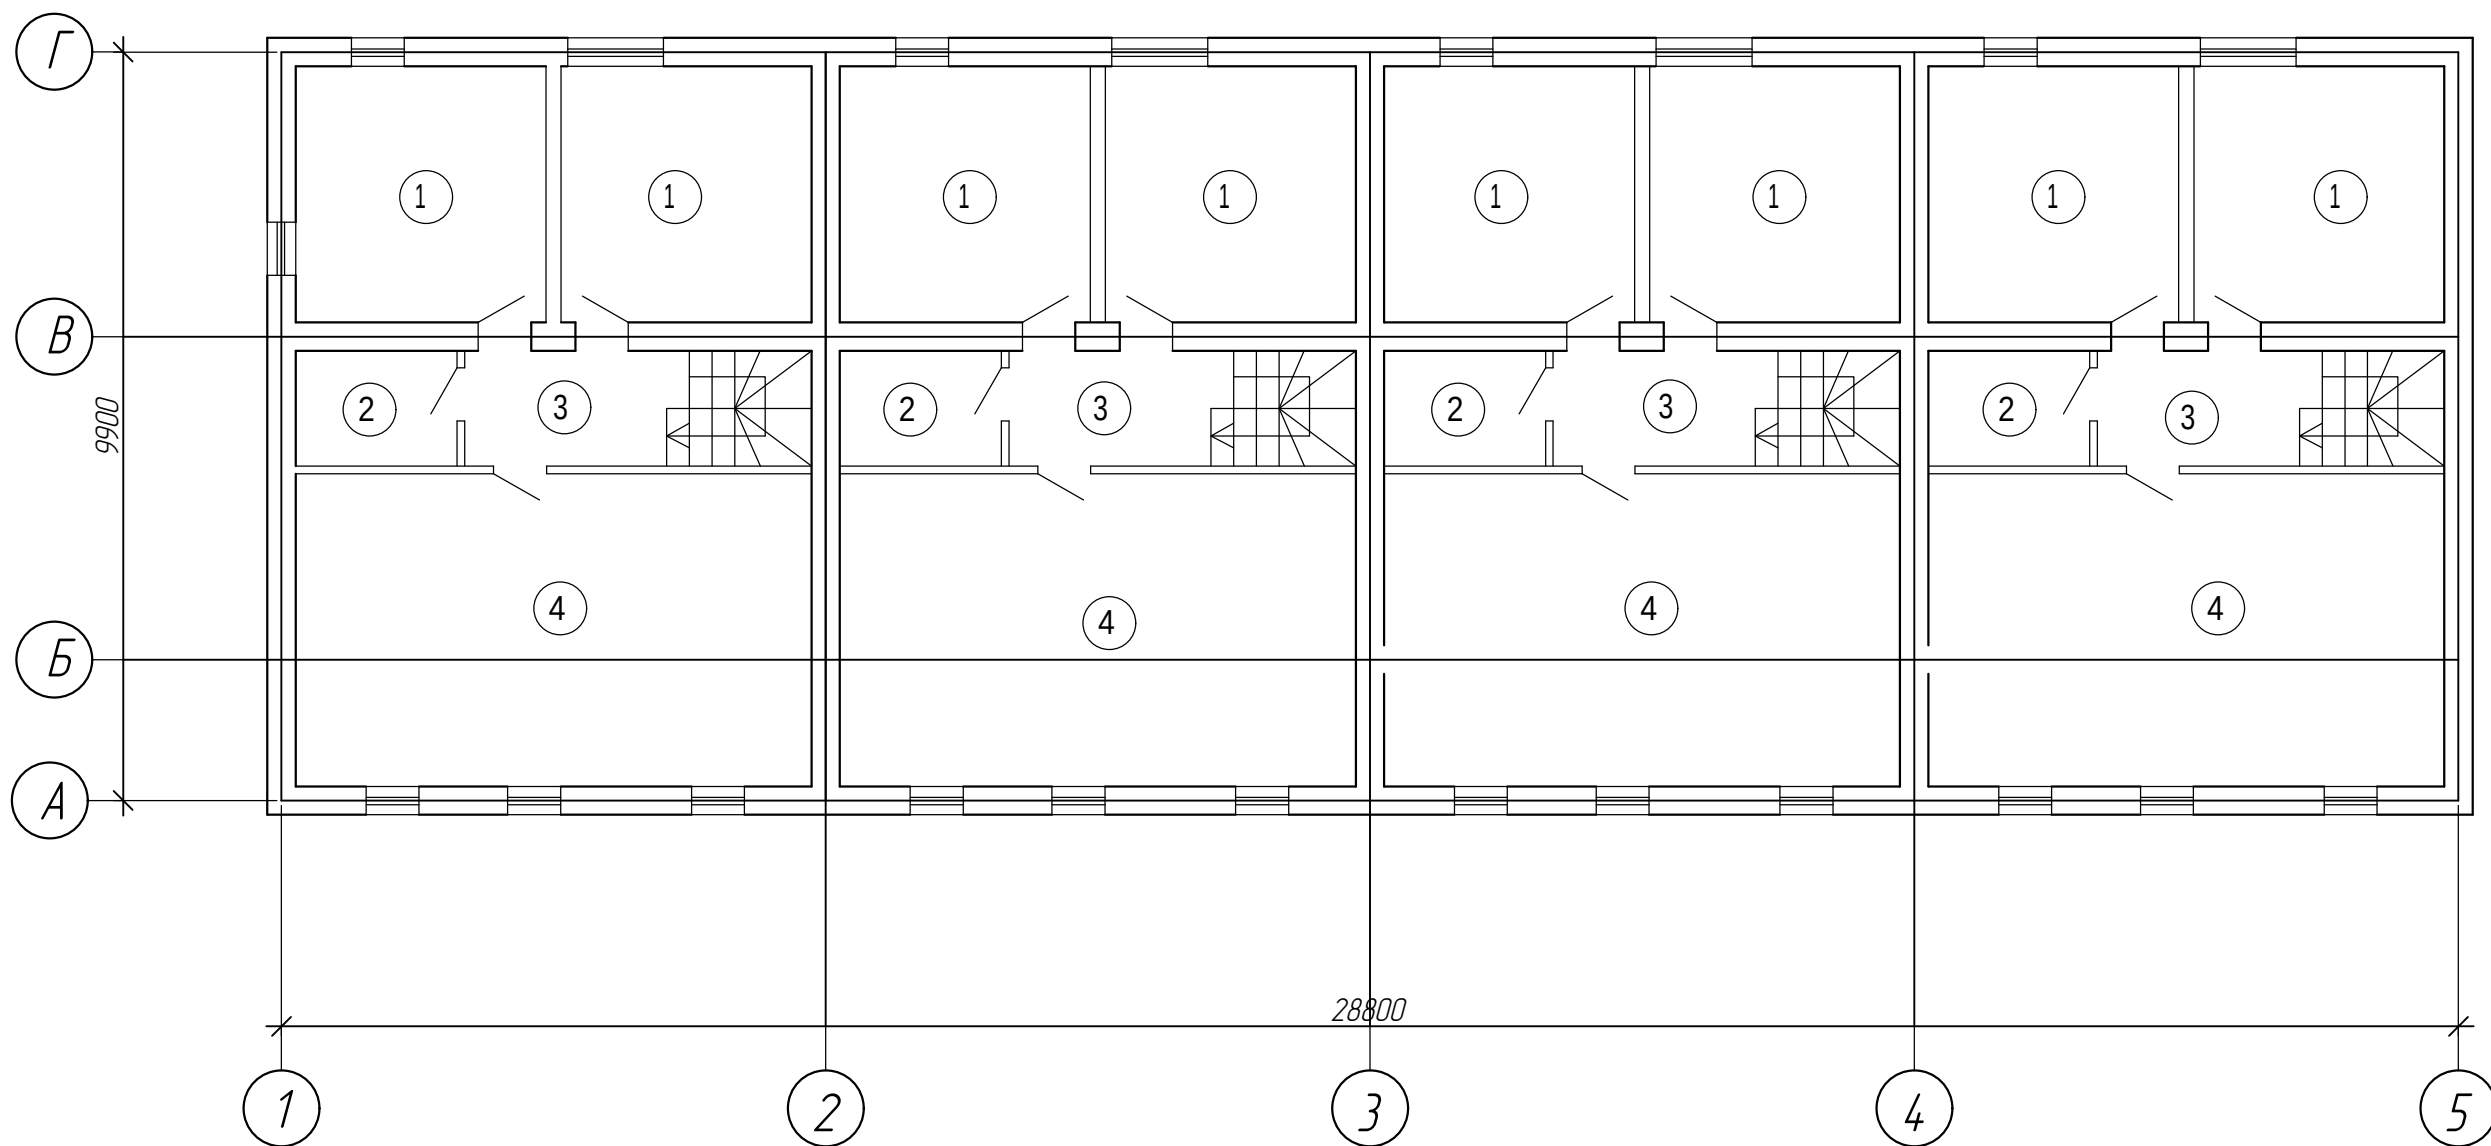

Экспликация помещений второго этажа

№ пом.	Наименование	Площадь м ²	Кат. пом.
1	Спальня	12,0	
2	С / у	4,6	
3	Холл	4,1	
4	Спальня	22,1	

    						01/26 - ПП			
						Пилотный проект коттеджного поселка в н.п. Б. Афанасово Нижнекамского района			
Изм.	Кол.	Лист	№ док	Подпись	Дата	4-х квартирный 2-х этажный жилой дом (таунхаус)	Стадия	Лист	Листов
Разраб.		Азлетдинова					П	10	
Проверил		Катаева				План 2-го этажа.	 АО "Нижнекамский Татагропромпроект"		
ГИП		Катаева							
Н. контр.		Наурова							
Гл. инж.		Ибрагимова							

4-х квартирный двухэтажный жилой дом.
3D вид.



- Наружные стены – газобетон 400 мм
Фасад – штукатурка, камень
Перекрытия – монолитные железобетонные
Отделка фасада – облицовочный материал
Полы – деревянные по лагам.
Крыша – чердачная
Кровля – металлочерепица
Фундаменты – монолитная ж/б плита

						01/26 – ПП			
						Пилотный проект коттеджного поселка в н.п. Б. Афанасово Нижнекамского района			
Изм.	Кол.	Лист	№ док	Подпись	Дата	4-х квартирный 2-х этажный жилой дом (таунхаус)	Стадия	Лист	Листов
Разраб.		Азлетдинава					П	11	
Проверил		Катаева				3D вид.	 АО "Нижнекамский Тазагропромпроект"		
ГИП		Катаева							
Н. контр.		Наурова							
Гл. инж.		Ибрагимова							

Здание бытового обслуживания.
3D вид в осях А – Д.

3D вид в осях А – Д, 5 – 1.






3D вид в осях А – Д, 5 – 1.







Согласовано:



Инв. № подл. Подпись и дата Взам. инв. №

 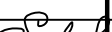 						01/26 – ПП			
						Пилотный проект коттеджного поселка в н.п. Б. Афанасово Нижнекамского района			
Изм.	Кол.	Лист	№ док.	Подпись	Дата	Здание бытового обслуживания.	Стадия	Лист	Листов
Разраб.		Азлетдинава					П	12	
Проверил		Катаева				3D виды.	 АО "Нижнекамский Татагропромпроект"		
ГИП		Катаева							
Н. контр.		Нацрова							
Гл. инж.		Ибрагимова							

Согласовано:

Инв. № подл. Подпись и дата Взам. инв. №

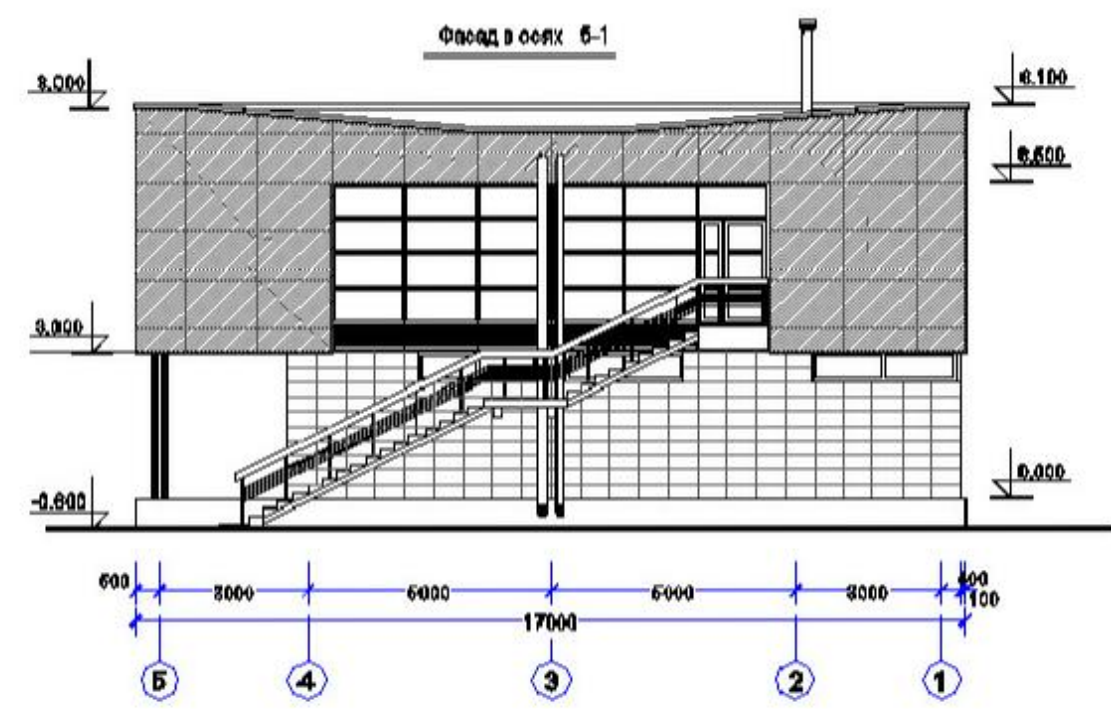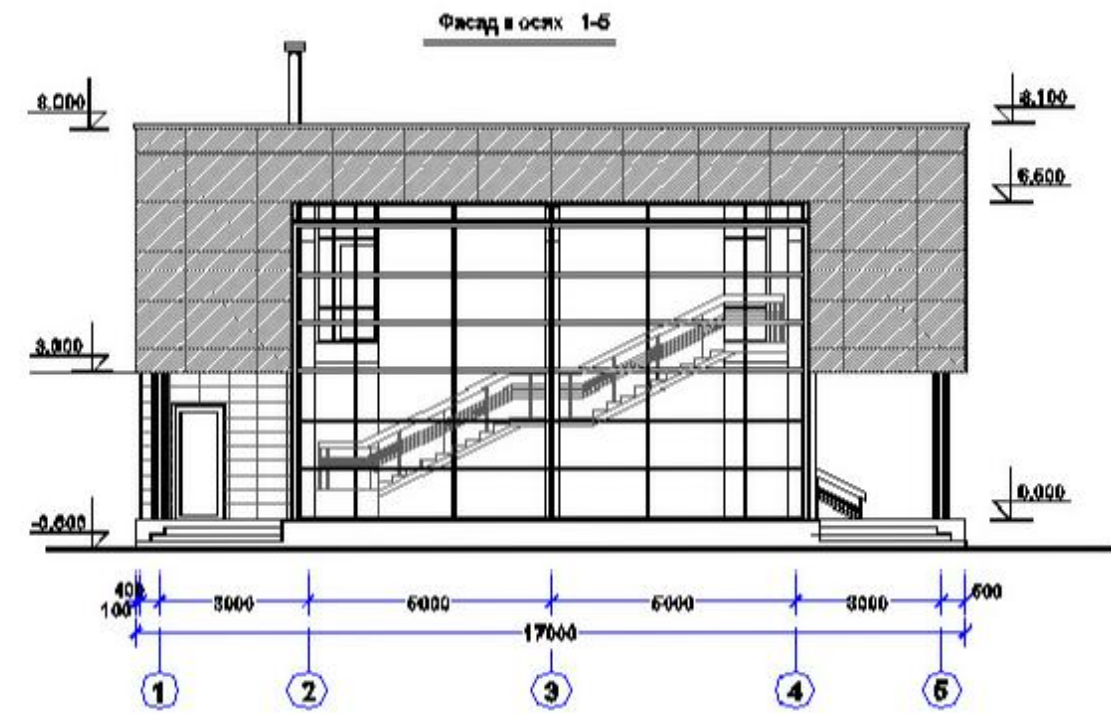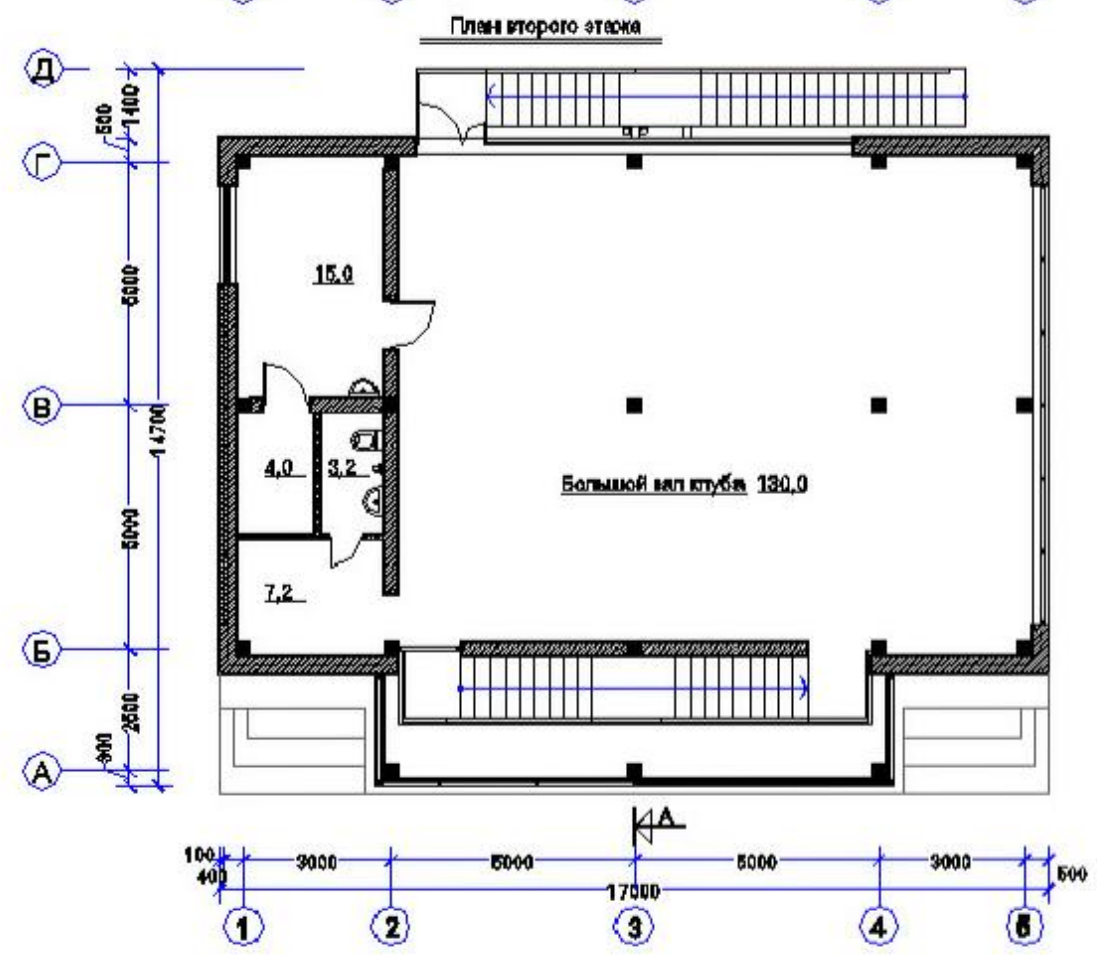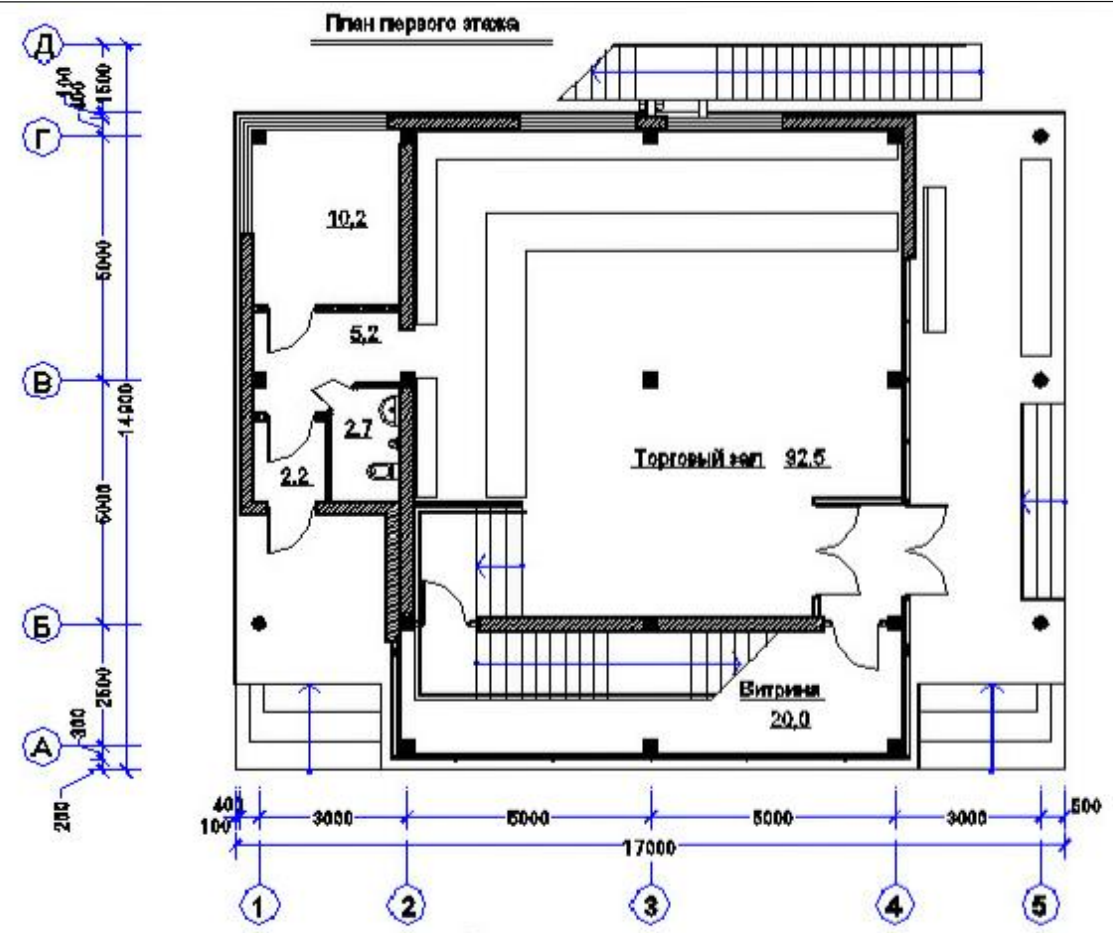

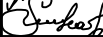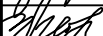						01/26 – ПП			
						Пилотный проект коттеджного поселка в н.п. Б. Афанасово Нижнекамского района			
Изм.	Кол.	Лист	№ док	Подпись	Дата	Здание бытового обслуживания.	Стадия	Лист	Листов
Разраб.		Азлетдинова					П	13	
Проверил		Катаева				Планы 1 и 2 этажа. Фасад 1-5, 5 -1.			АО "Нижнекамский Татагропромпроект"
ГИП		Катаева							
Н. контр.		Наурова							
Гл. инж.		Ибрагимова							

Детский сад –школа на 120 мест .

3D вид.



3D вид.




Согласовано:

Инв. № подл. Подпись и дата Взам. инв. №

						01/26 – ПП			
						Пилотный проект коттеджного поселка в н.п. Б. Афанасово Нижнекамского района			
Изм.	Кол.	Лист	№ док	Подпись	Дата	Детский сад – школа на 120 мест.	Стадия	Лист	Листов
Разраб.		Азлетдинава					П	14	
Проверил		Катаева				3D виды.	 АО "Нижнекамский Татагропромпроект"		
ГИП		Катаева							
Н. контр.		Нацурова							
Гл. инж.		Ибрагимова							

План 1-го этажа.

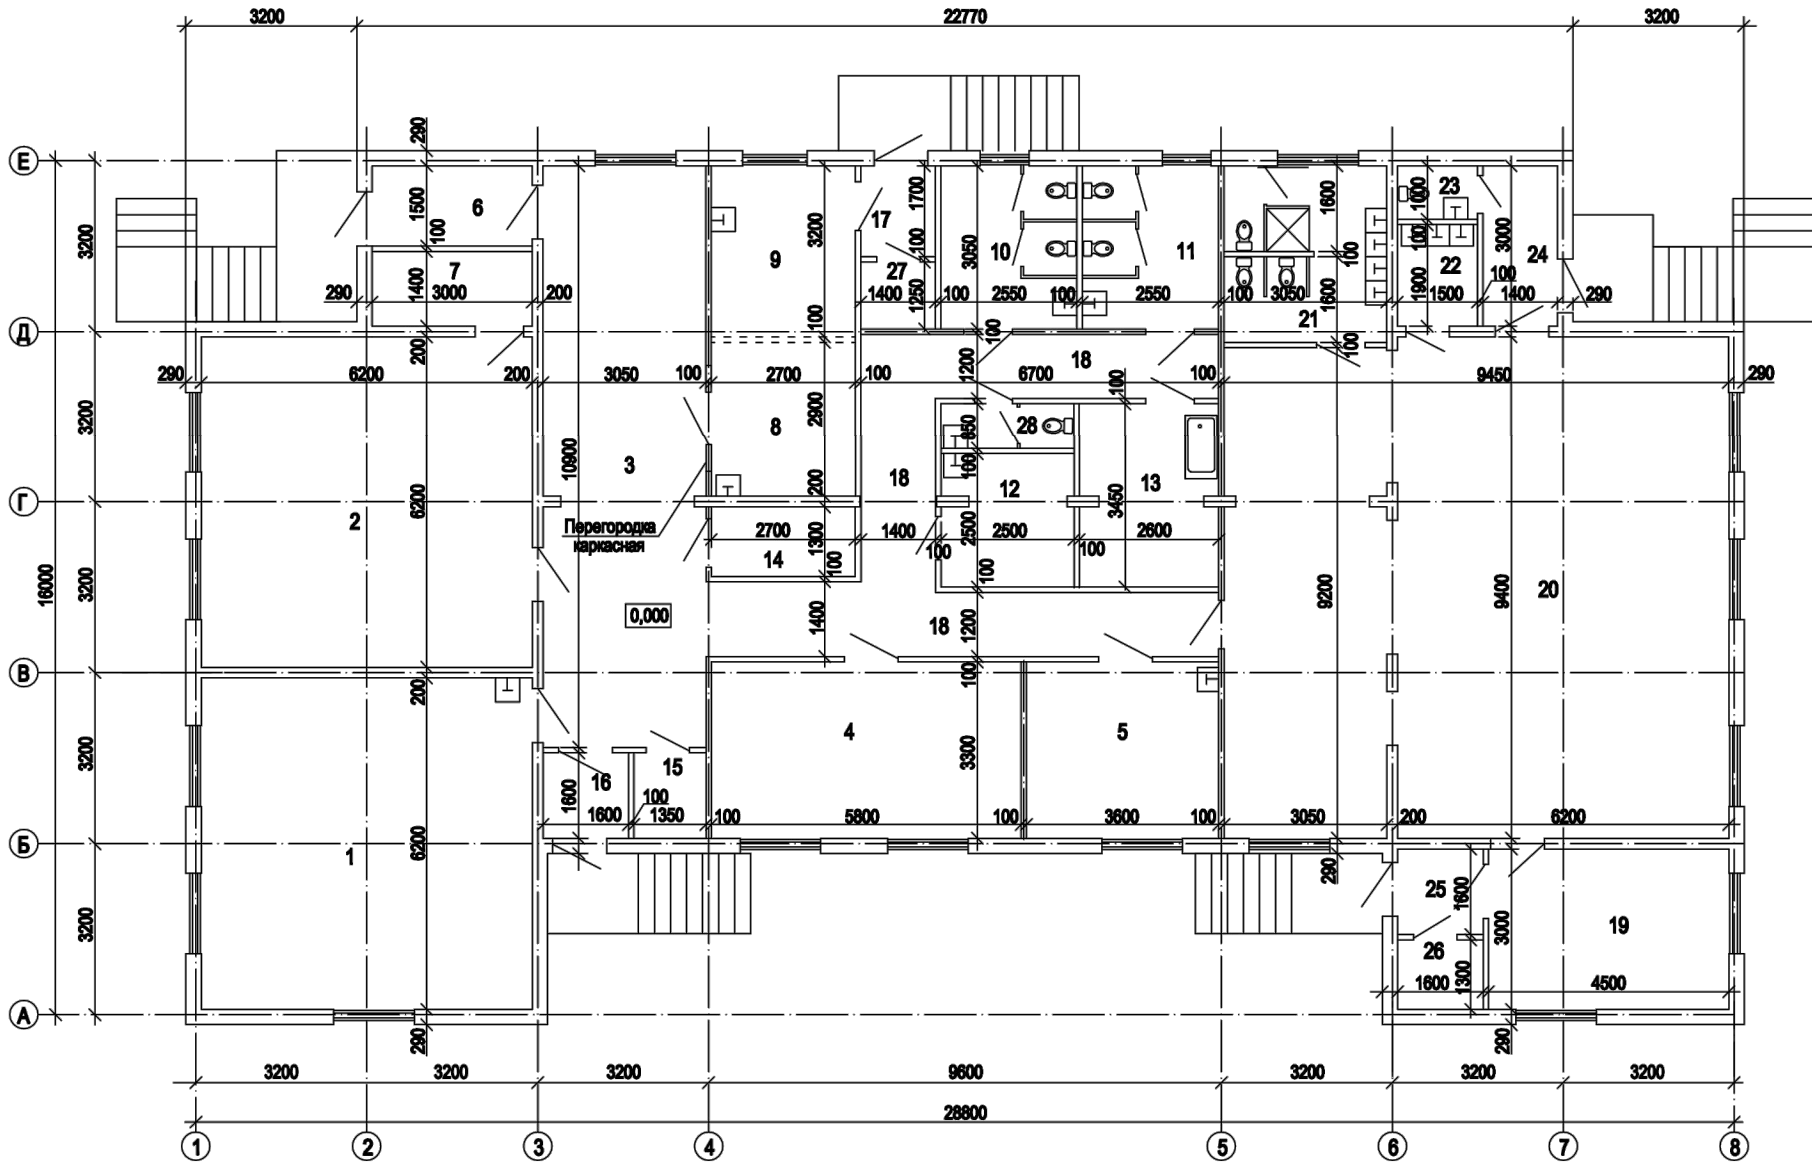

Экспликация помещений

№ пом.	Наименование	Площадь м2	Кат. пом.
1	Учебный класс	38,4	
2	Зал музыкальных занятий и физической подготовки	38,4	
3	Рекреация	33,2	
4	Учительская	19,1	
5	Медкабинет	11,9	
6	Тамбур	4,5	
7	Инвентарная	4,2	
8	Столовая	7,8	
9	Пищеблок	8,6	
10	Туалет	7,8	
11	Туалет	7,8	
12	Кладовая для уборочного инвентаря	6,1	
13	Постирочная	8,8	
14	Электрощитовая	3,5	
15	Гардероб	2,2	
16	Тамбур	2,6	
17	Загрузочная пищеблока	2,4	
18	Коридор	25,2	
19	Раздевальная	13,5	
20	Групповая со спальней зоной	87,4	
21	Туалетная	9,9	
22	Буфетная	2,8	
23	Туалет	1,5	
24	Тамбур	4,2	
25	Тамбур	2,5	
26	Кладовая	2,1	
27	Хозкладовая	1,7	
28	Туалет для персонала	2,1	
		360,2	

Согласовано:


Инв. № подл. Подпись и дата Взам. инв. №

										01/26 - ПП
										Пилотный проект коттеджного поселка в н.п. Б. Афанасово Нижнекамского района
Изм.	Кол.	Лист	№ док	Подпись	Дата					
Разраб.				Азлетдинава						
Проверил				Катаева						
										Детский сад - школа на 120 мест.
										Стадия Лист Листов
										П 15
ГИП				Катаева						
Н. контр.				Наурова						
Гл. инж.				Ибрагимова						
										План 1-го этажа.
										АО "Нижнекамский Татагропромпроект"


проект мечети «Азиз-60»



План 1-го этажа

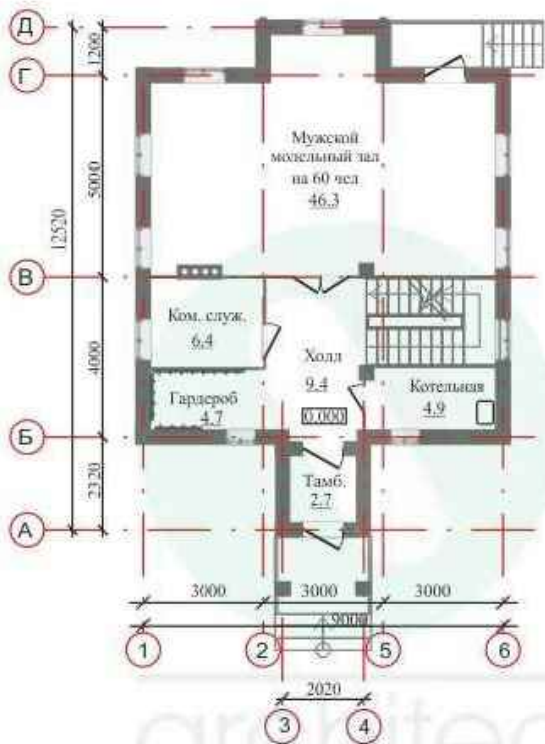

План балкона

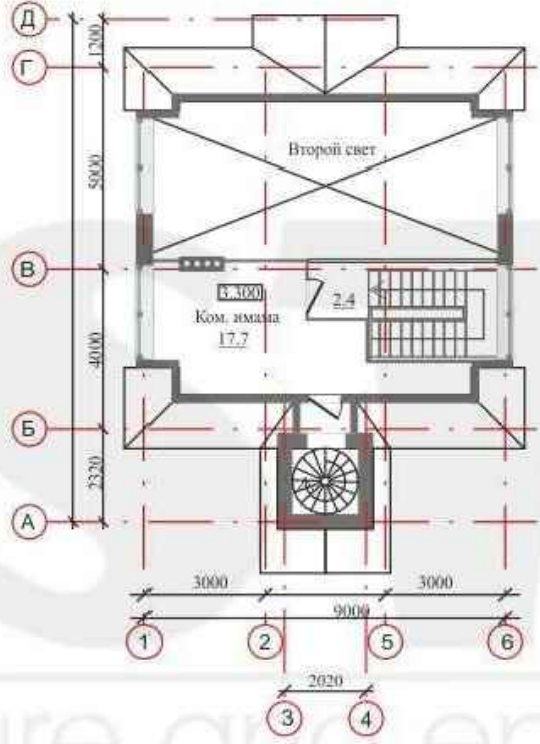

План цокольного этажа



Мечеть на 60 посетителей, выполнена в классическом стиле. Габариты здания 9м x 13 м. Наружные стены выполнены в штукатурке. Кровля скатная с применением металлочерепицы. В цокольном этаже имеется универсальный зал, который может использоваться как женский зал, учебный класс, так и для проведения различных мероприятий. Данный вид проекта подходит для сельских местностей и пригородов и малых городов.

Согласовано:

Инв. № подл. Взам. инв. № Подпись и дата

						01/26 - ПП			
						Пилотный проект коттеджного поселка в н.п. Б. Афанасово Нижнекамского района			
Изм.	Кол.	Лист	№ док	Подпись	Дата	Мечеть на 60 посетителей.	Стадия	Лист	Листов
Разраб.		Азлетдинова					П	16	
Проверил		Катаева				План 1-го и 2-го этажей. 3 D виды.	 АО "Нижнекамский Татагропромпроект"		
ГИП		Катаева							
Н. контр.		Наурова							
Гл. инж.		Ибрагимова							